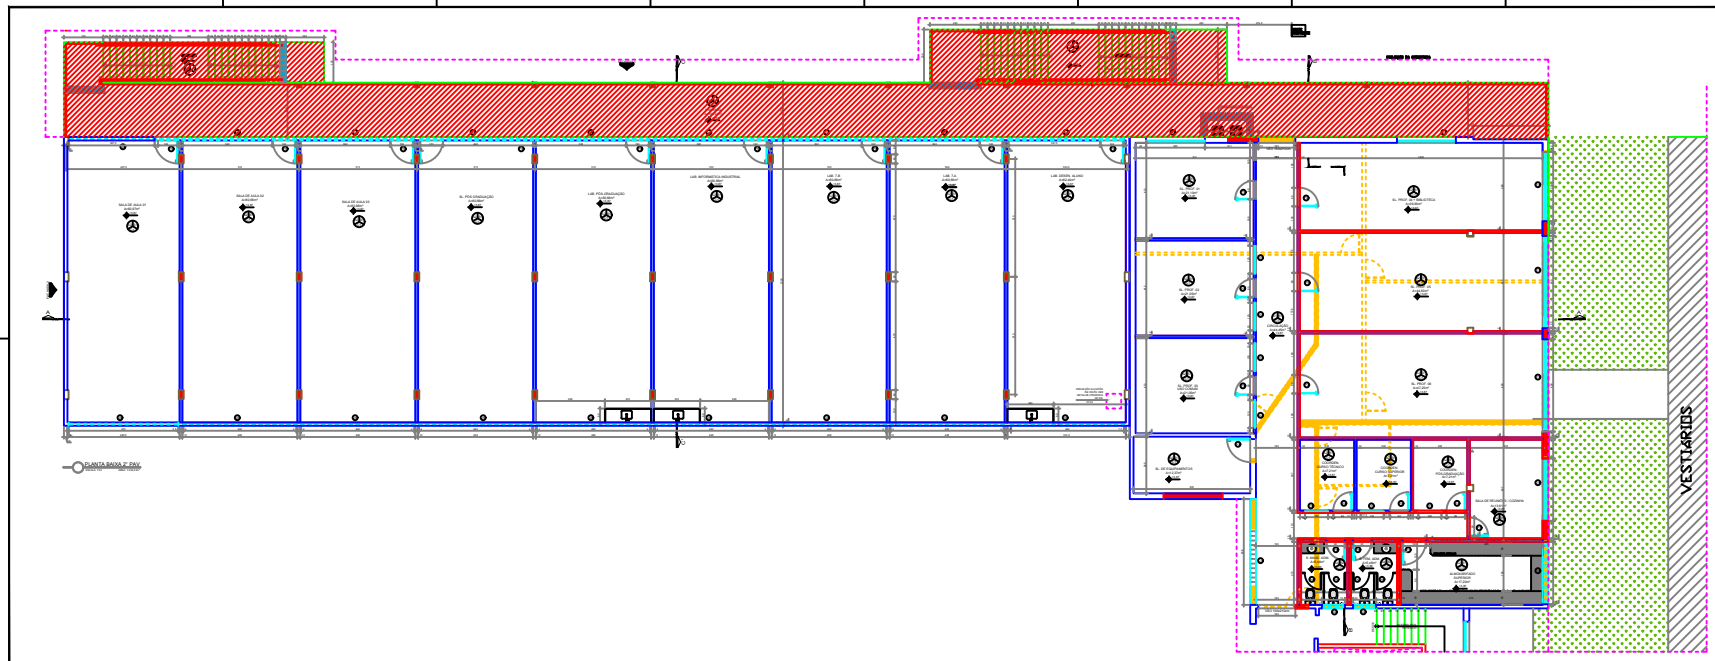
VESTIÁRIOS
PLANTA BAIXA 2º PAV.
QUADRO DE ESQUADRIAS
QUADRO DE REVESTIMENTO INTERNO
LEGENDA
IFES - INSTITUTO FEDERAL DO ESPÍRITO SANTO
CAMPUS VITÓRIA
AVANTEC ENGENHARIA Ltda.
PROJETO DE REFORMA DO BLOCO M
PROJETO ARQUITETÔNICO
PLANTA BAIXA 2º PAVT.
04/12

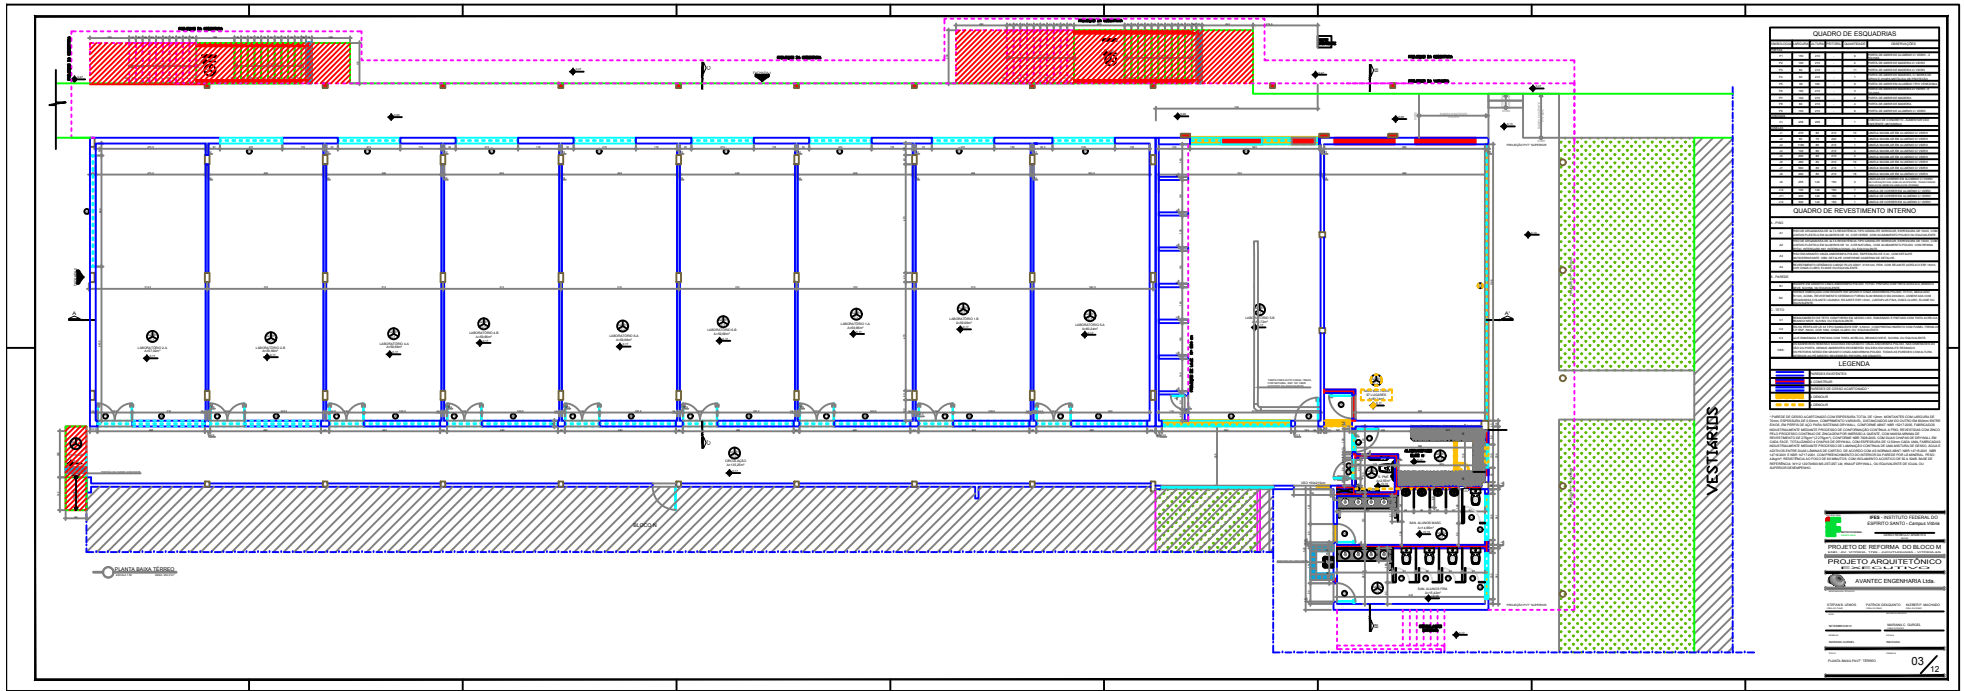
VESTIÁRIOS
PLANTA BAIXA TÉRREO
QUADRO DE ESQUADRIAS
QUADRO DE REVESTIMENTO INTERNO
LEGENDA
IFES - INSTITUTO FEDERAL DO ESPÍRITO SANTO - Campus Vitória
AVANTEC ENGENHARIA Ltda.
PROJETO DE REFORMA DO BLOCO M
PROJETO ARQUITETÔNICO
PLANTA BAIXA PAVT. TÉRREO
03/12